



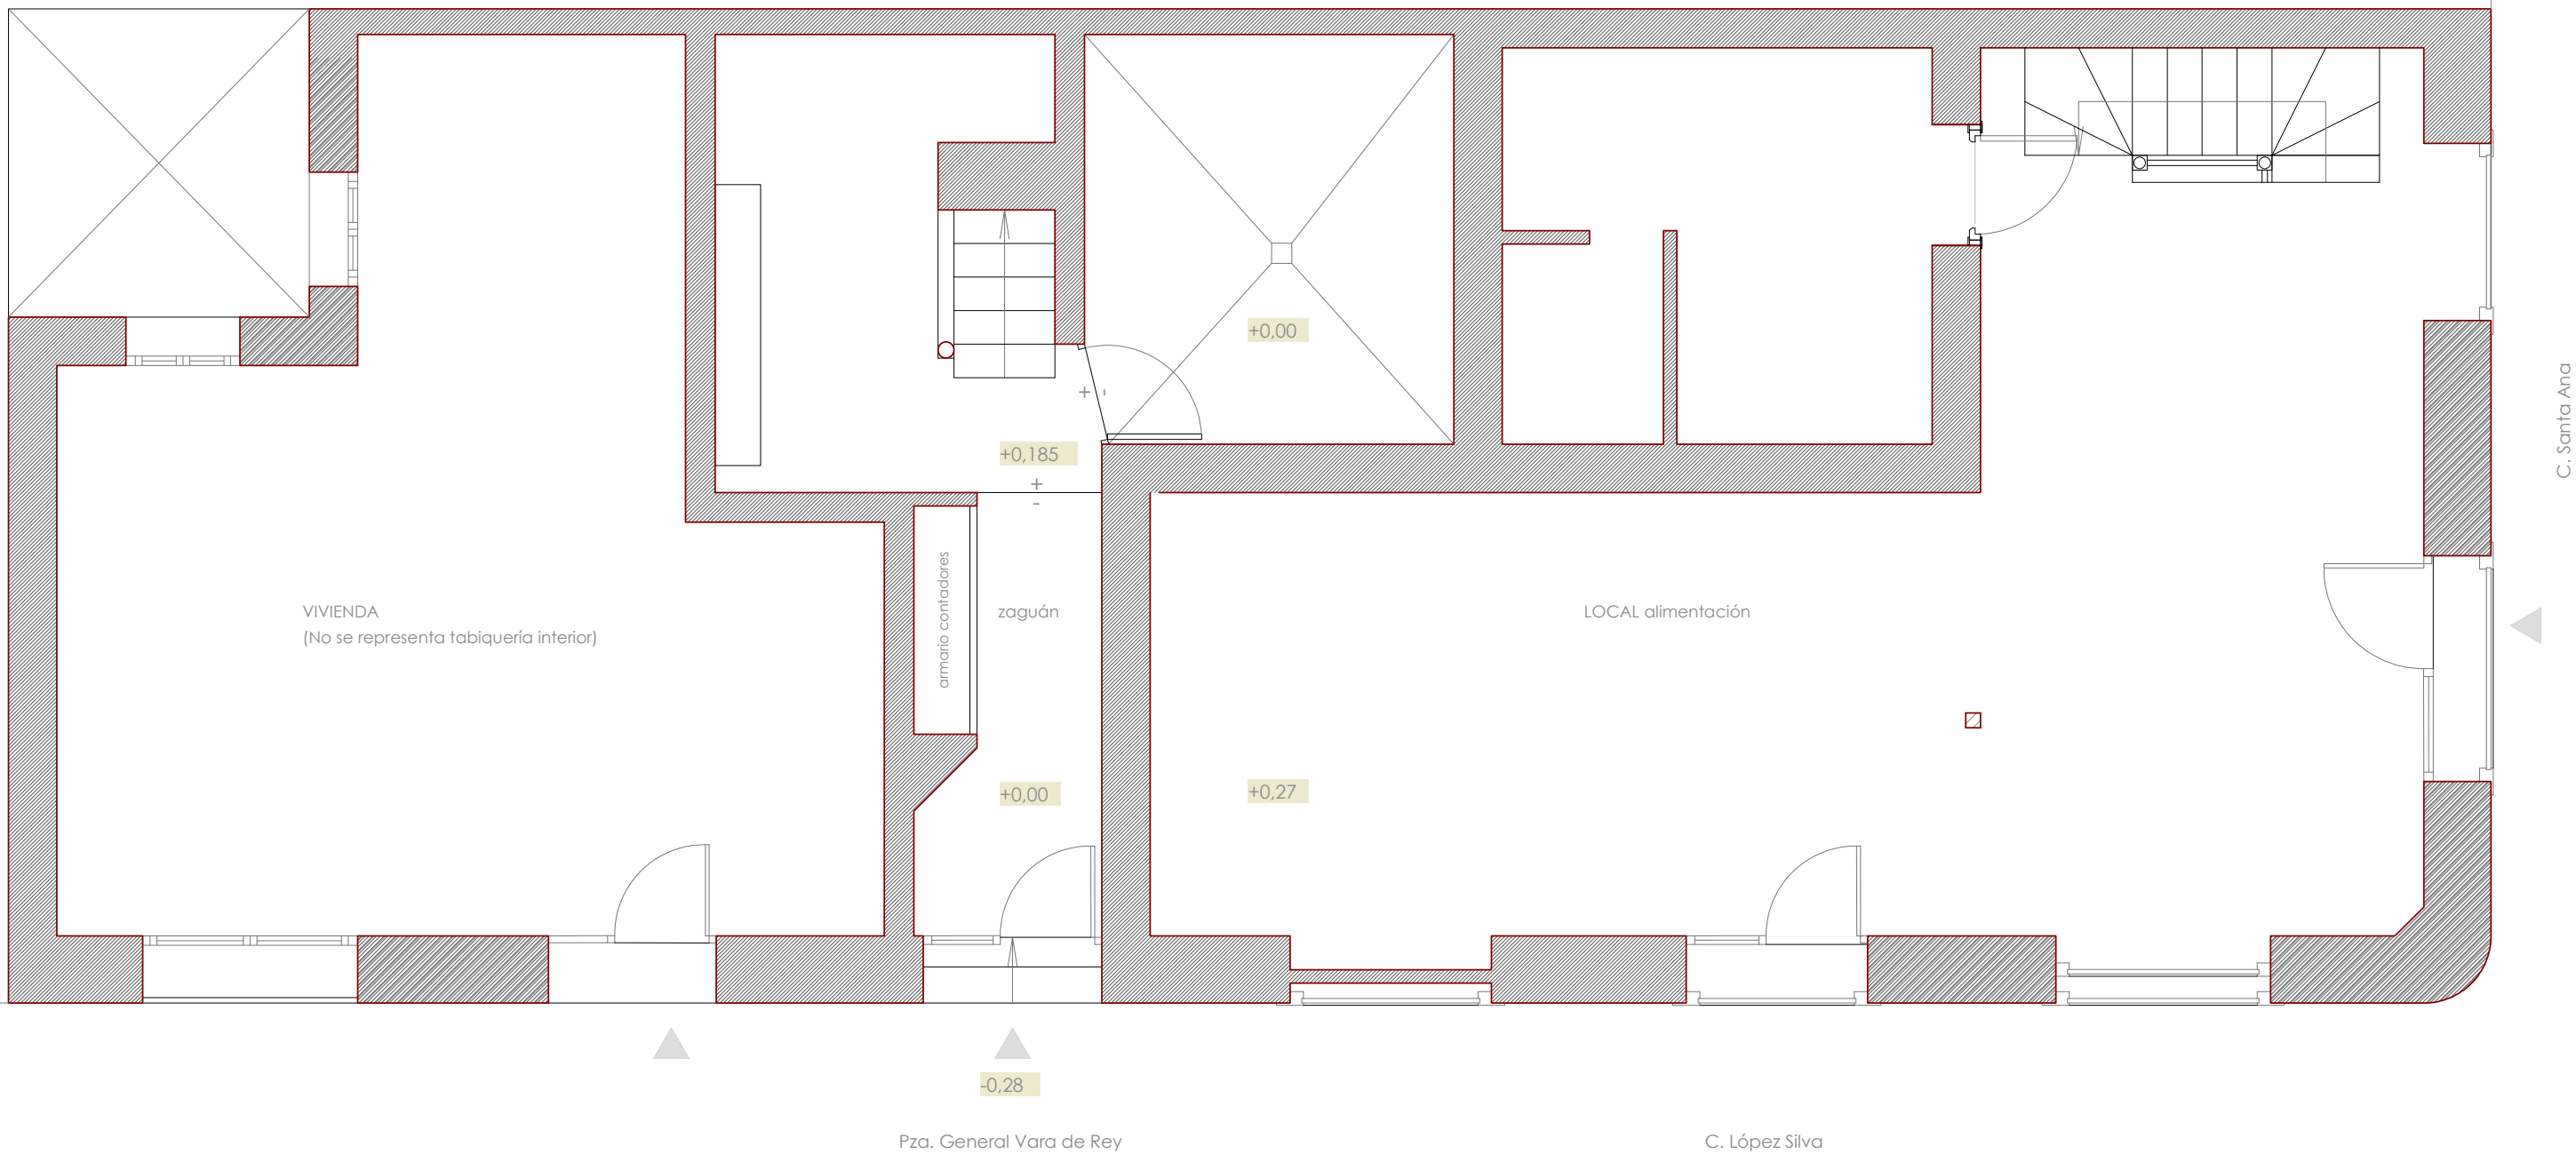

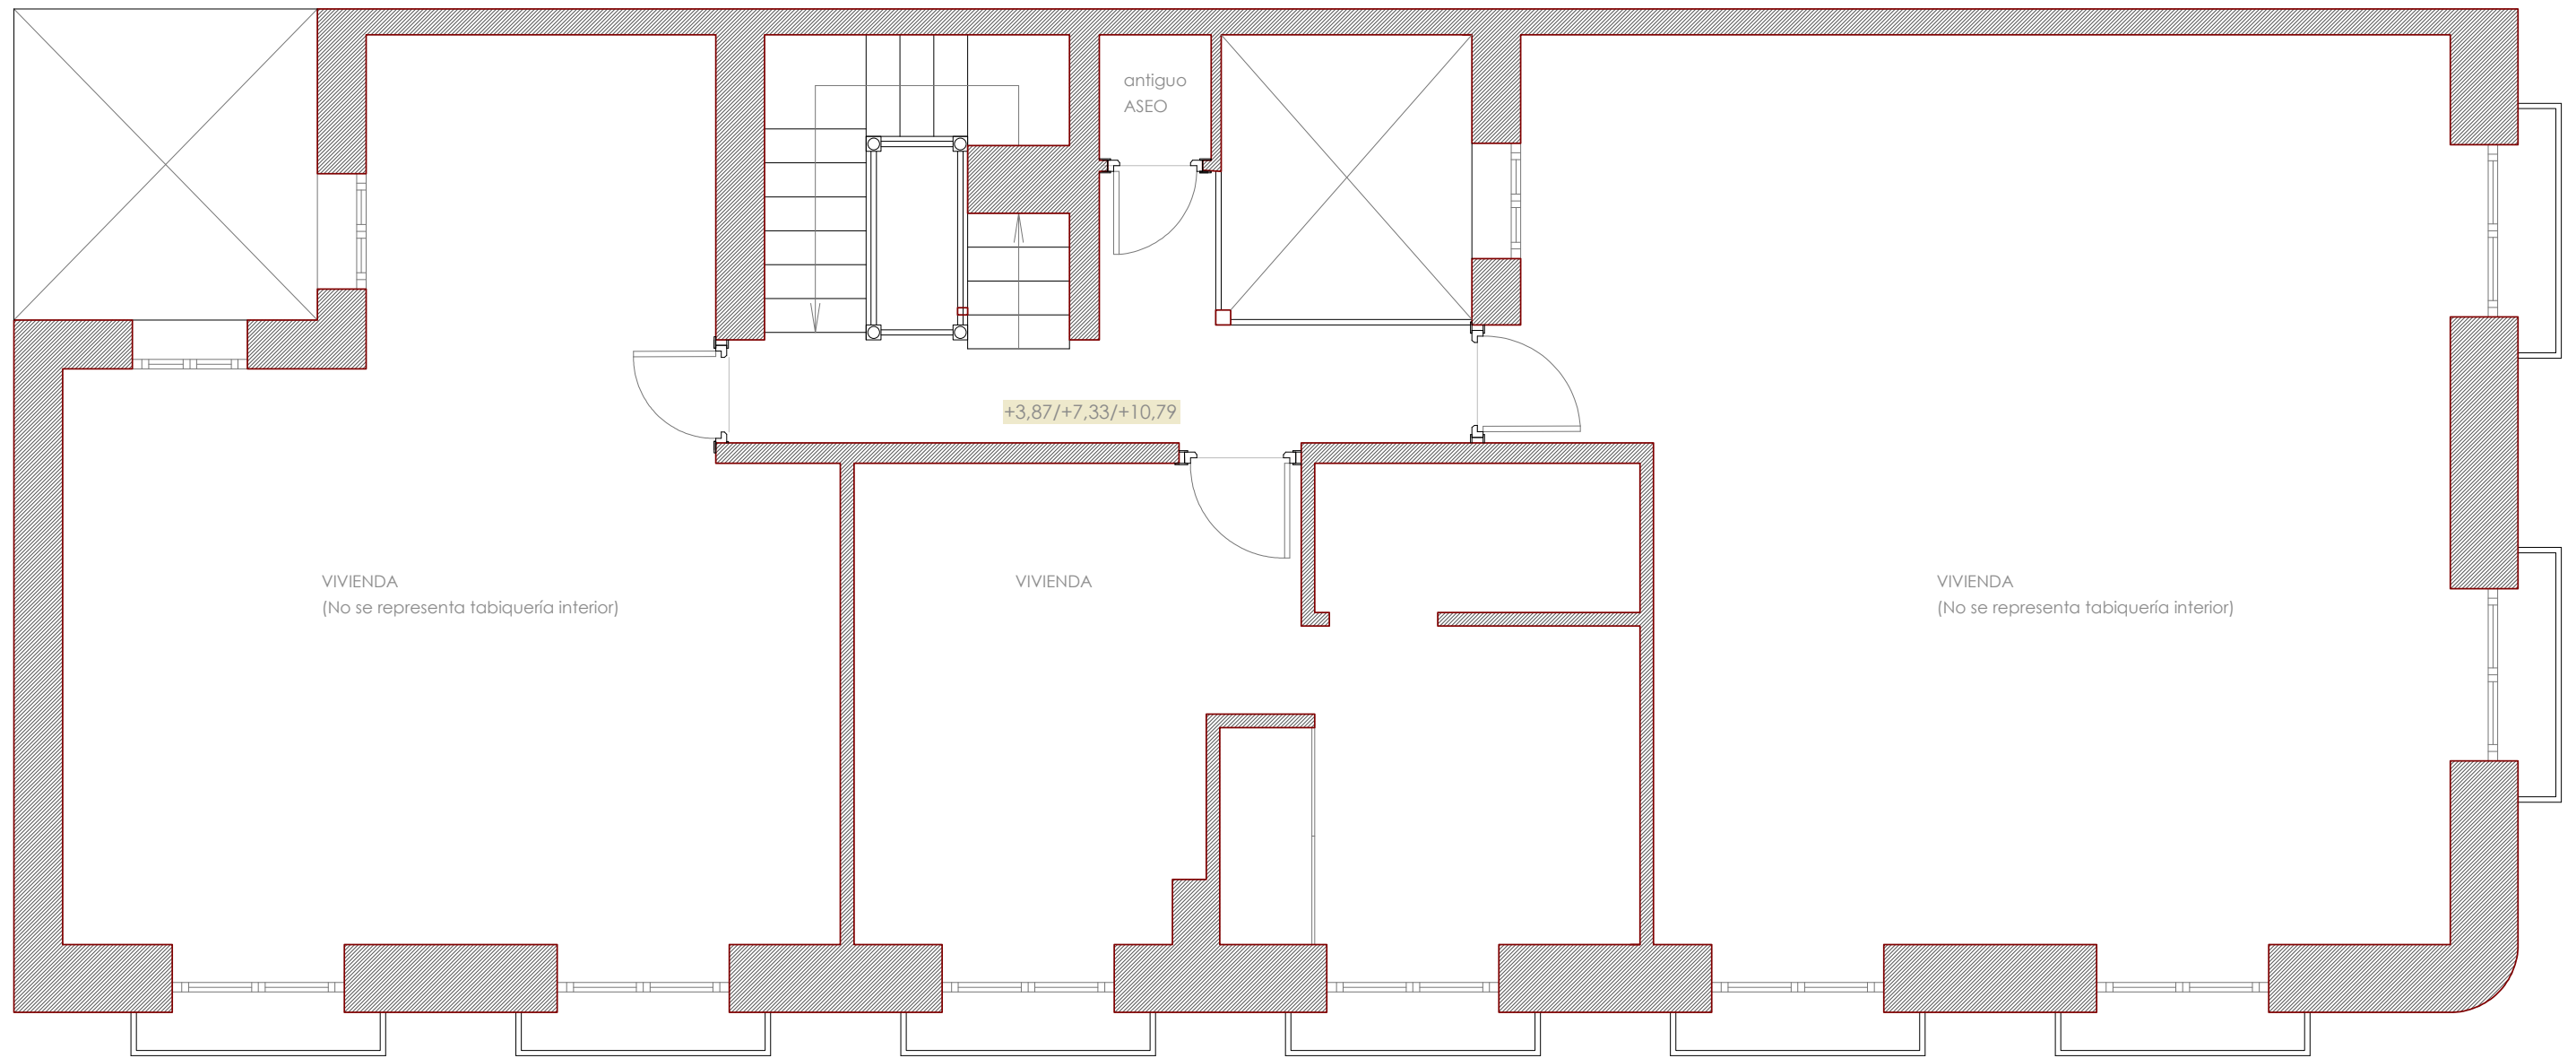



ALZADO A PZA. GENERAL VARA DE REY

Proyecto básico de MEJORA DE LA ACCESIBILIDAD UNIVERSAL

Pza. General Vara de Rey, 10, Madrid

propiedad:

C.P. General Vara de Rey, 10

arquitecto:

Luis Fernando Carretero Marco col. 20024

1:75
DIN A3

E. ACTUAL/REFORMADO
ALZADOS (I)

A3

Alacet Arquitectura SL. Tr. Cañuelo, 4. Valverde de Alcalá

alacet.

10/01/2025



ALZADO A C. SANTA ANA

Alacet Arquitectura SL. Tr. Cañuelo, 4. Valverde de Alcalá

alacet.

Proyecto básico de MEJORA DE LA ACCESIBILIDAD UNIVERSAL

Pza. General Vara de Rey, 10, Madrid

propiedad:

C.P. General Vara de Rey, 10

arquitecto:

Luis Fernando Carretero Marco col. 20024


1:75

DIN A4

E. ACTUAL/REFORMADO
ALZADOS (II)

10/01/2025

A4

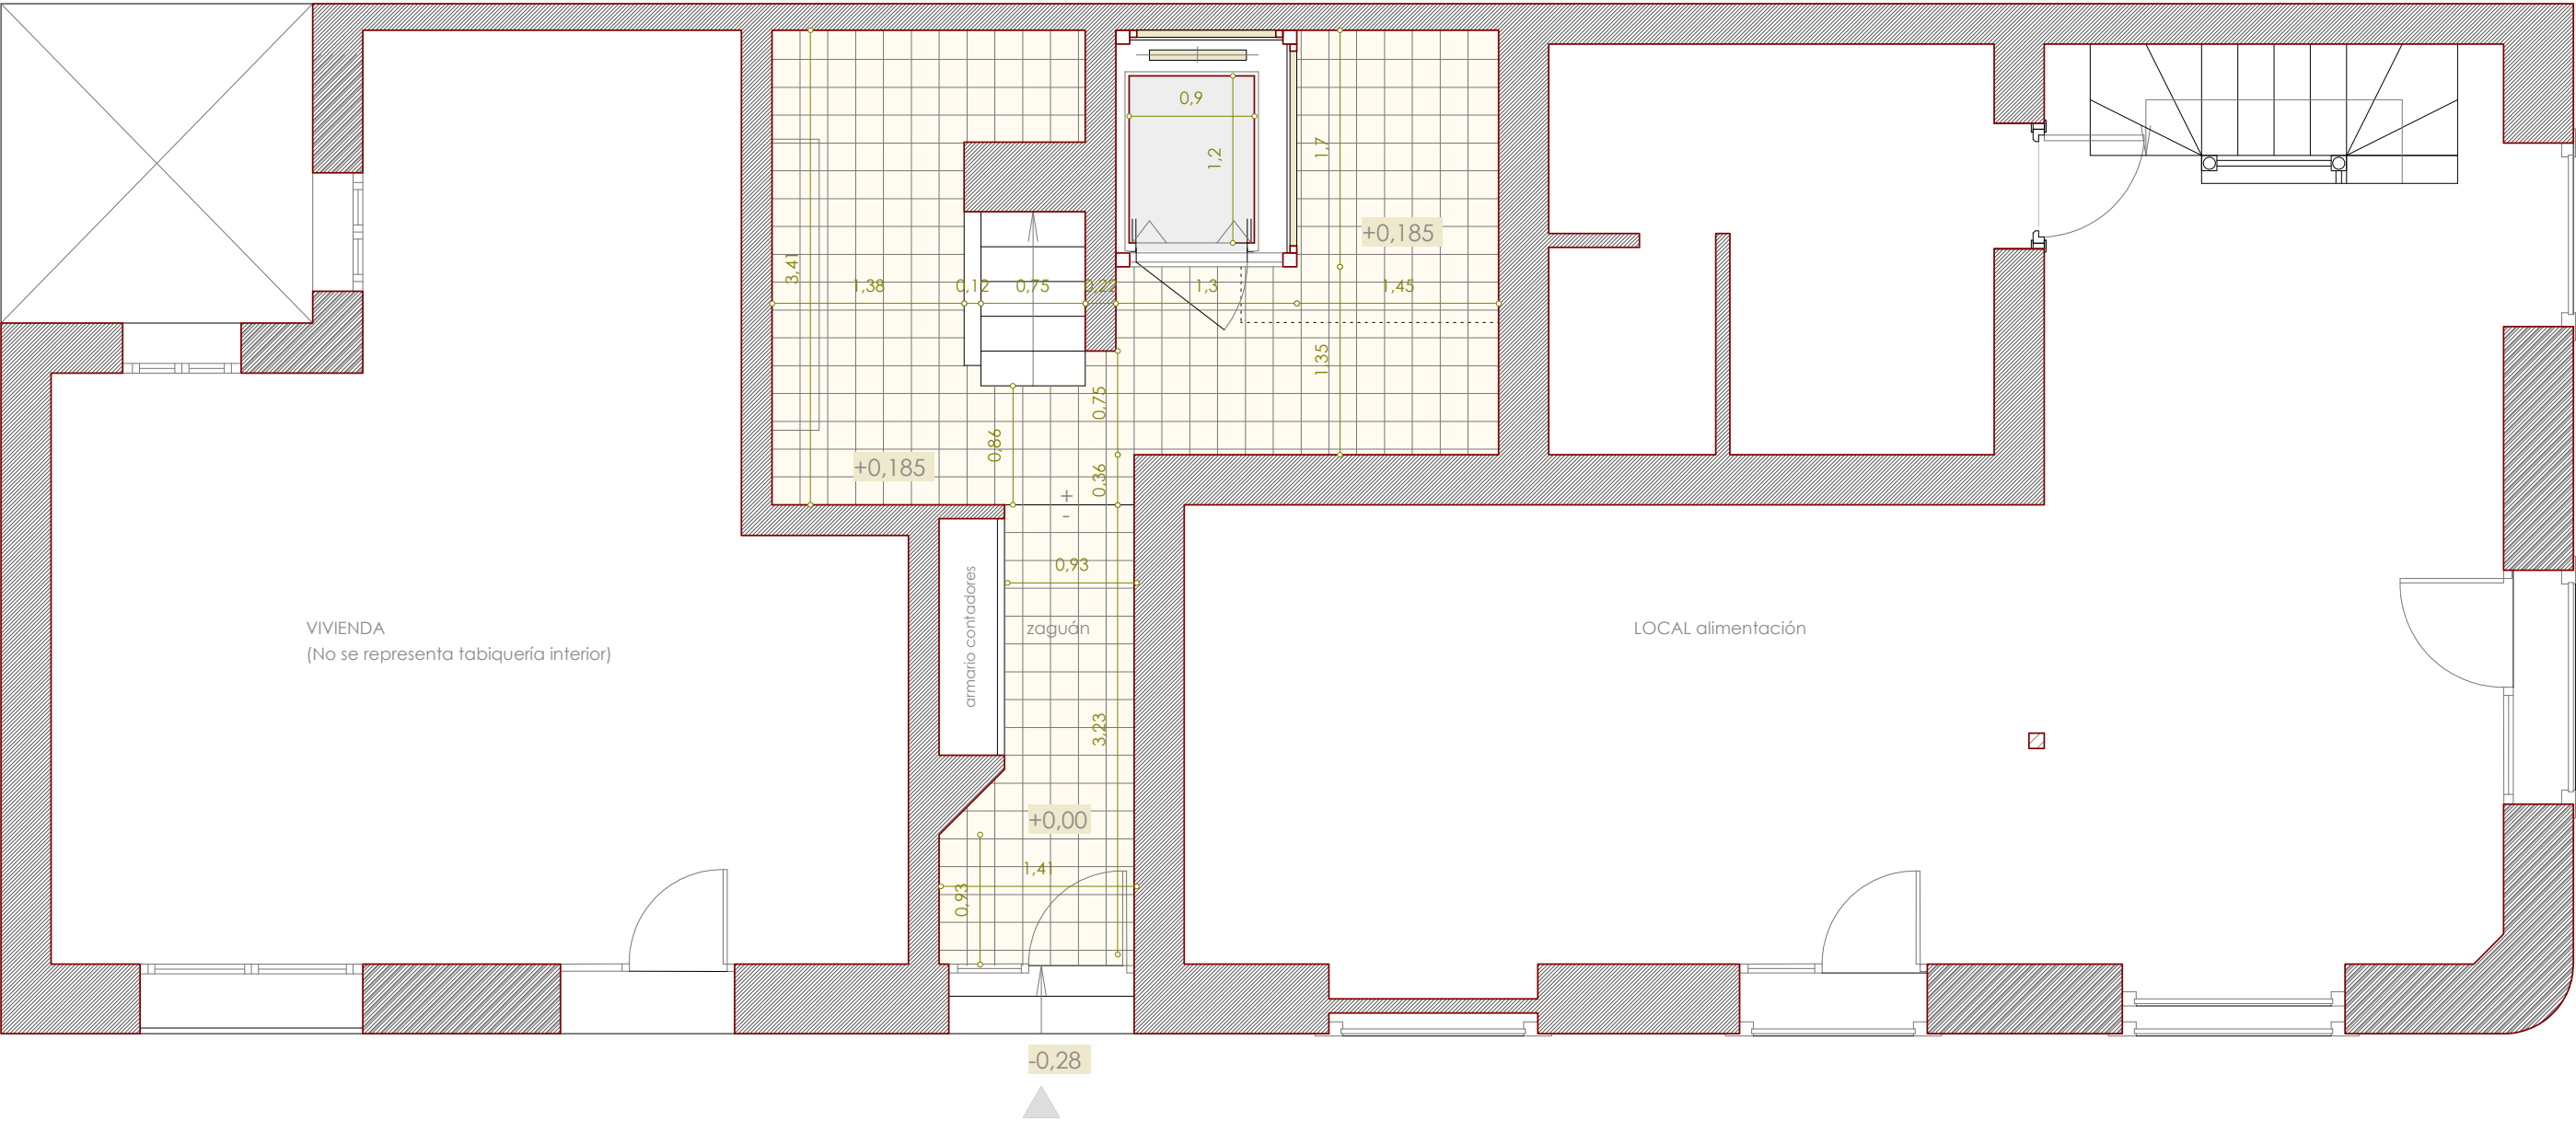

INTERVENCIONES

- A1-** Vaciado de tierras y formación de estructura de foso de hormigón armado, de profundidad máxima de 1 m.

A2- Eliminación de peldaño existente entre cota de patio y la de arranque de escalera, mediante recrecido en zona de patio, y eliminación de puerta practicable preexistente. Incluso formación de pendientes y dotación de canaleta de desagüe.


A3- Instalación de ascensor eléctrico, con cinco paradas, de dimensiones de cabina de 90x120cm de planta y 220cm de altura, con puertas de acceso plegables tipo bus, de 80cm de ancho libre, sobre nueva estructura metálica de torre, de lado exterior de 170 x 130cm, y 17,27 m de altura total, a base de perfiles metálicos atornillados, lacados en color RAL 1013 (blanco perla) para estructura vertical y parteluces y 7002 (gris oliva) para junquillos, cuajado mediante vidrio laminar transparente, con puertas de planta vidriadas practicables.

A4- Solado de conjunto de zaguán en planta baja, mediante gres semimanual Montserrat de Calaf, 20x20cm, rojo.
- A5-** Reubicación de placa botonera exterior de portero automático, a altura accesible (80-120cm).

A10- Adaptaciones en falsos techos de galería de planta 4ª, alrededor de coronación de estructura de torre de ascensor, y rascado, emplastecido y pintura de conjunto de techos, en plantas baja a 4ª, mediante revestimiento al temple balco,

A11- Aplicación de revestimiento de pintura al silicato, sobre paramentos verticales de patio y galerías, incluso rascado y regularización previa de superficies.

A12- Aplicación de revestimiento de pintura al temple, sobre paramentos verticales de caja de escaleras y zaguán de planta baja, en color similar al existente, y aplicación de esmalte sintético sobre frisos de base, color marrón similar al existente, previa reposición de zonas faltantes y emplastecido de zonas dañadas.

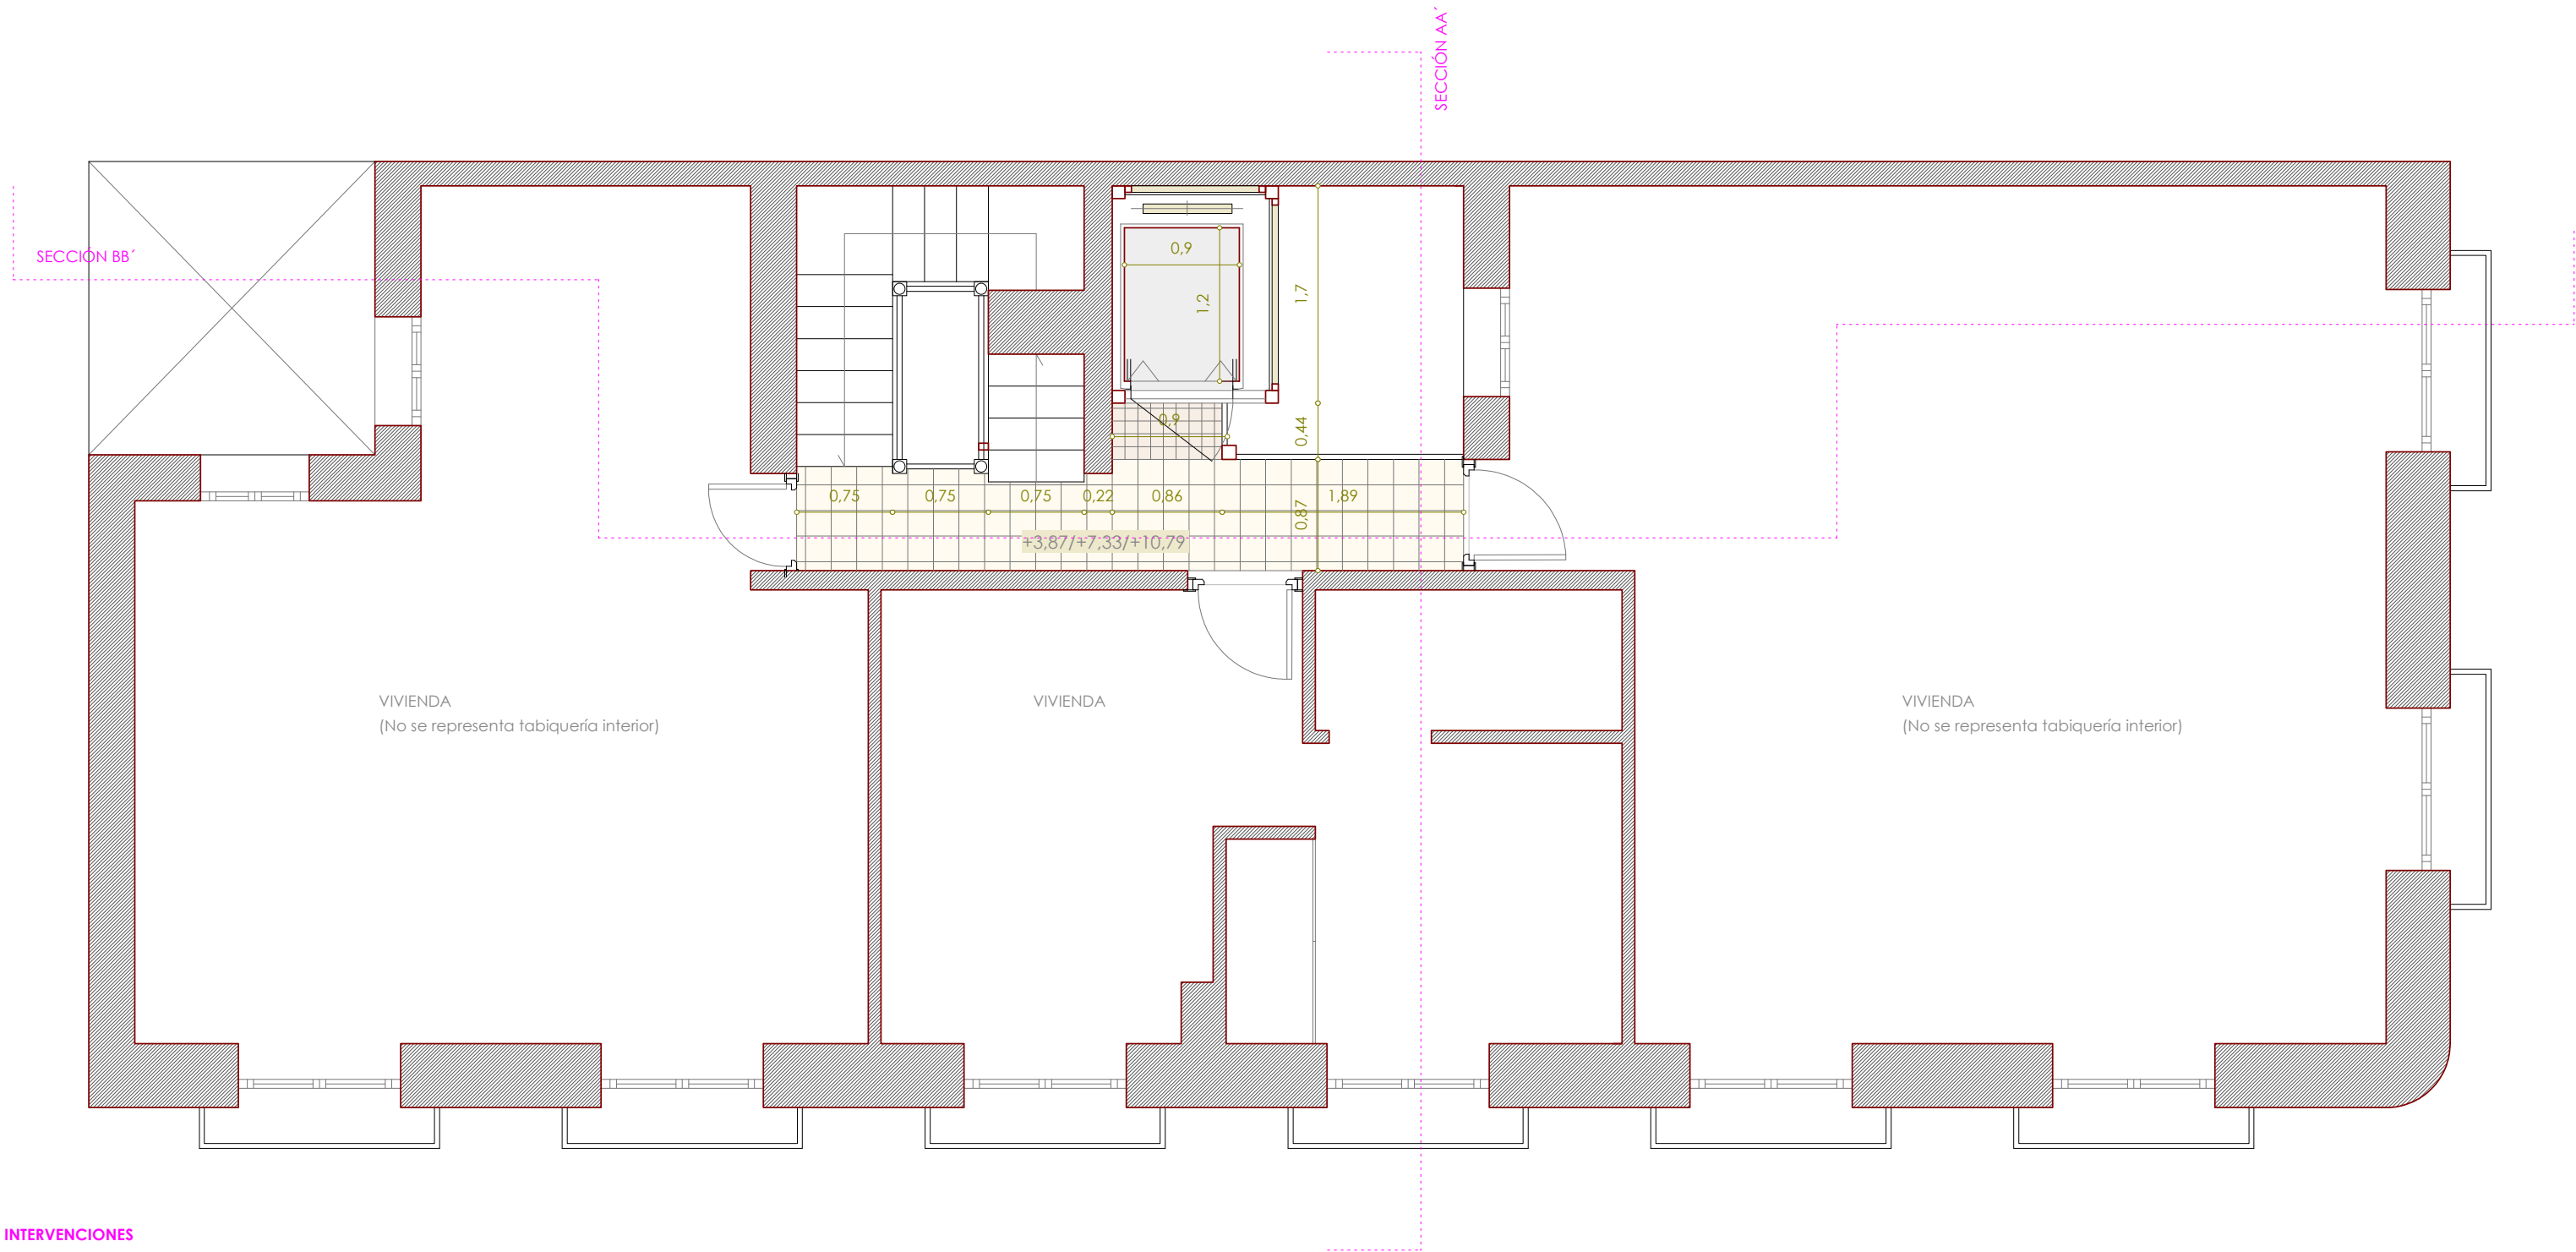

INTERVENCIONES

A3- Instalación de ascensor eléctrico, con cinco paradas, de dimensiones de cabina de 90x120cm de planta y 220cm de altura, con puertas de acceso plegables tipo bus, de 80cm de ancho libre, sobre nueva estructura metálica de torre, de lado exterior de 170 x 130cm, y 17,27 m de altura total, a base de perfiles metálicos atornillados, lacados en color RAL 1013 (blanco perla) para estructura vertical y paneluces y 7002 (gris oliva) para junquillos, cuajado mediante vidrio laminar transparente, con puertas de planta vidriadas practicables.

A6- Demolición de caras expuestas de aseos en plantas 1ª a 4ª (cara de acceso y cara a patio), de un pie de ladrillo macizo, incluso parte proporcional de entramado de madera, y posterior picado y regularización de paramento vertical continuo resultante, en altura completa. Incluso retirada parcial de barandillas.

A7- Demolición de tramo de forjado en plantas 1ª a 4ª, en zona correspondiente a aseos, incluso retirada de parte proporcional de carreras de madera.

A8- Formación de nuevo recrecido en piso de distribuidores de plantas, para regularización de nivel, y solado mediante gres semimanual Montserrat de Calaf, 20x20cm, rojo.

A9- Construcción de pasarela ligera, con piso formado por bandejas de chapa plegada perforada, sobre perfiles metálicos tubulares. Con barandilla a base de pletinas planas en barrotos y pasamanos. Lacado RAL

A10- Adaptaciones en falsos techos de galería de planta 4ª, alrededor de coronación de estructura de torre de ascensor, y rascado, emplastecido y pintura de conjunto de techos, en plantas baja a 4ª, mediante revestimiento al temple balnco,

A11- Aplicación de revestimiento de pintura al silicato, sobre paramentos verticales de patio y galerías, incluso rascado y regularización previa de superficies.


A12- Aplicación de revestimiento de pintura al temple, sobre paramentos verticales de caja de escaleras y zaguán de planta baja, en color similar al existente, y aplicación de esmalte sintético sobre frisos de base, color marrón similar al existente, previa reposición de zonas faltantes y emplastecido de zonas dañadas.

Proyecto básico de MEJORA DE LA ACCESIBILIDAD UNIVERSAL				10/01/2025
Pza. General Vara de Rey, 10, Madrid				
propiedad:	arquitecto:	1:50	ESTADO REFORMADO	A6
C.P. General Vara de Rey, 10	Luis Fernando Carretero Marco col. 20024	DIN A3		

Alacet Arquitectura SL, Tr. Cañuelo, 4, Valverde de Alcalá

alacet.

A6

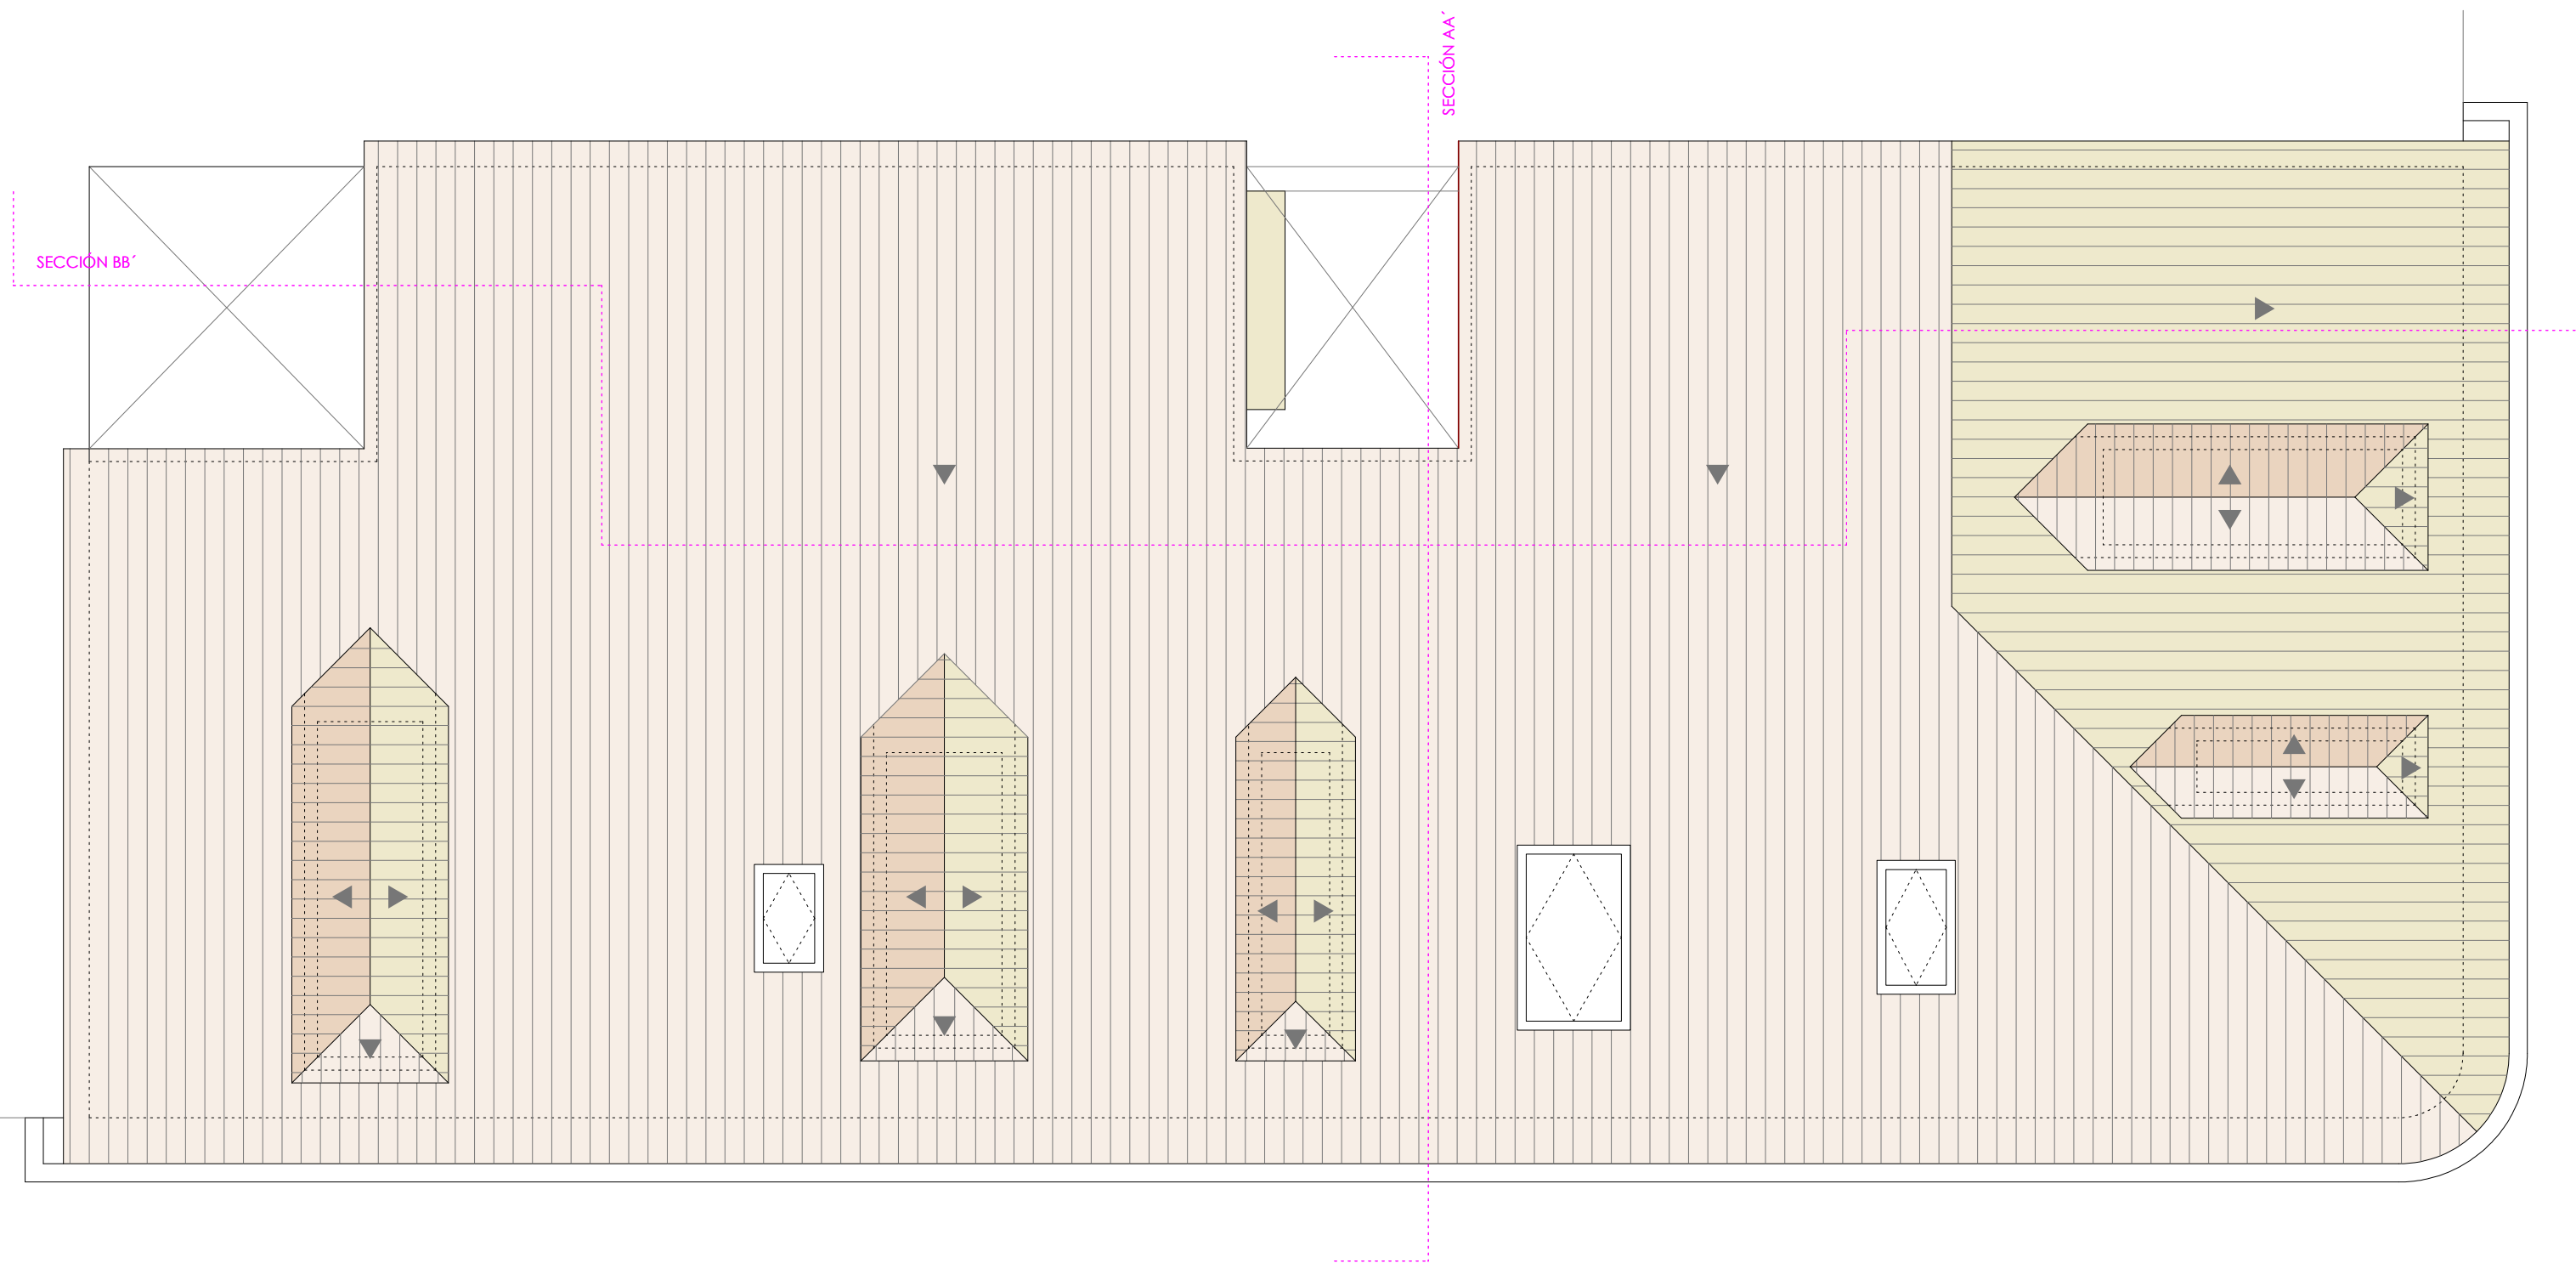

Proyecto básico de MEJORA DE LA ACCESIBILIDAD UNIVERSAL

Pza. General Vara de Rey, 10, Madrid

propiedad:

C.P. General Vara de Rey, 10

arquitecto:

Luis Fernando Carretero Marco col. 20024

1:50
DIN A3




ESTADO REFORMADO
PLANTA CUBIERTA

10/01/2025

A7

Alacet Arquitectura SL, Tr. Cañuelo, 4, Valverde de Alcalá

alacet.

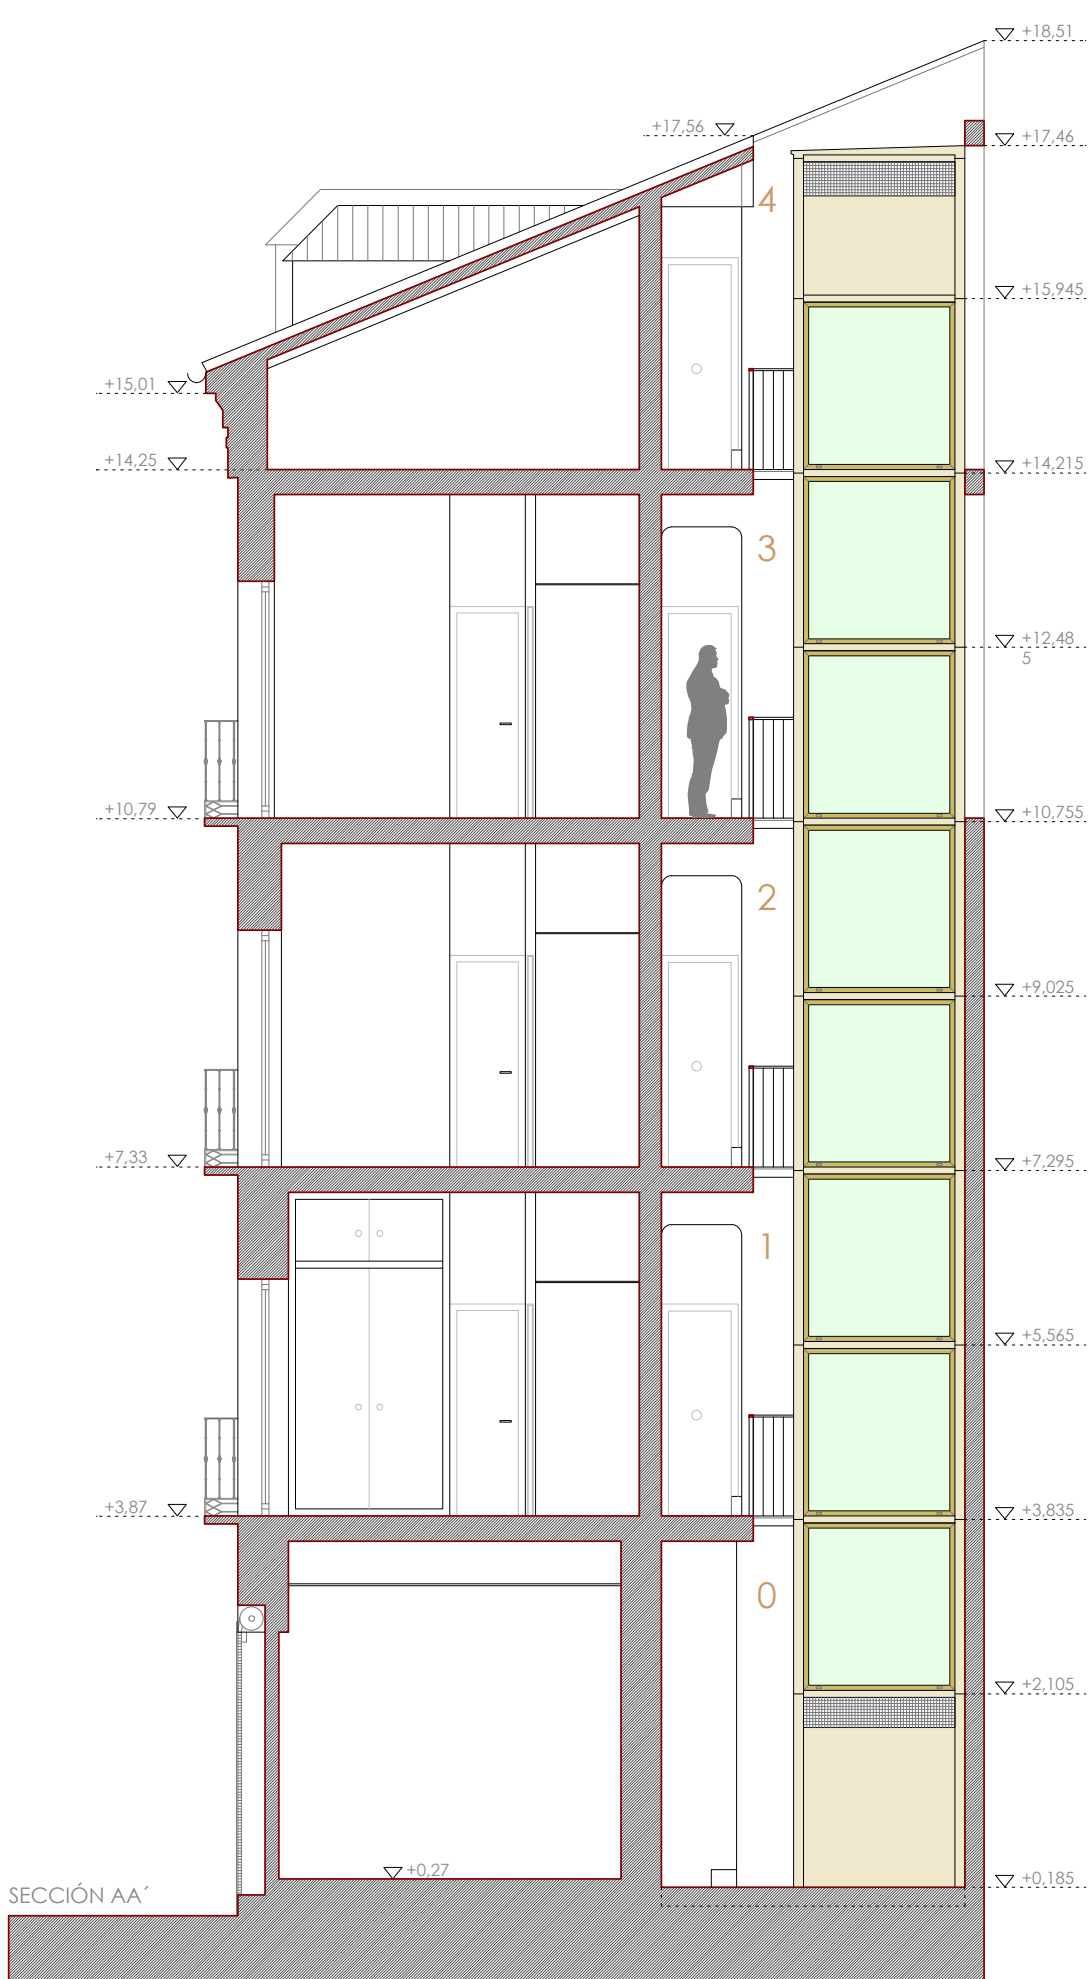

Alacet Arquitectura SL. Tr. Cañuelo, 4. Valverde de Alcalá

alacet.

Proyecto básico de MEJORA DE LA ACCESIBILIDAD UNIVERSAL

Pza. General Vara de Rey, 10, Madrid

10/01/2025

propiedad:

arquitecto:

1:75

ESTADO REFORMADO


C.P. General Vara de Rey, 10

Luis Fernando Carretero Marco col. 20024

DIN A4

SECCIONES (I)

A8

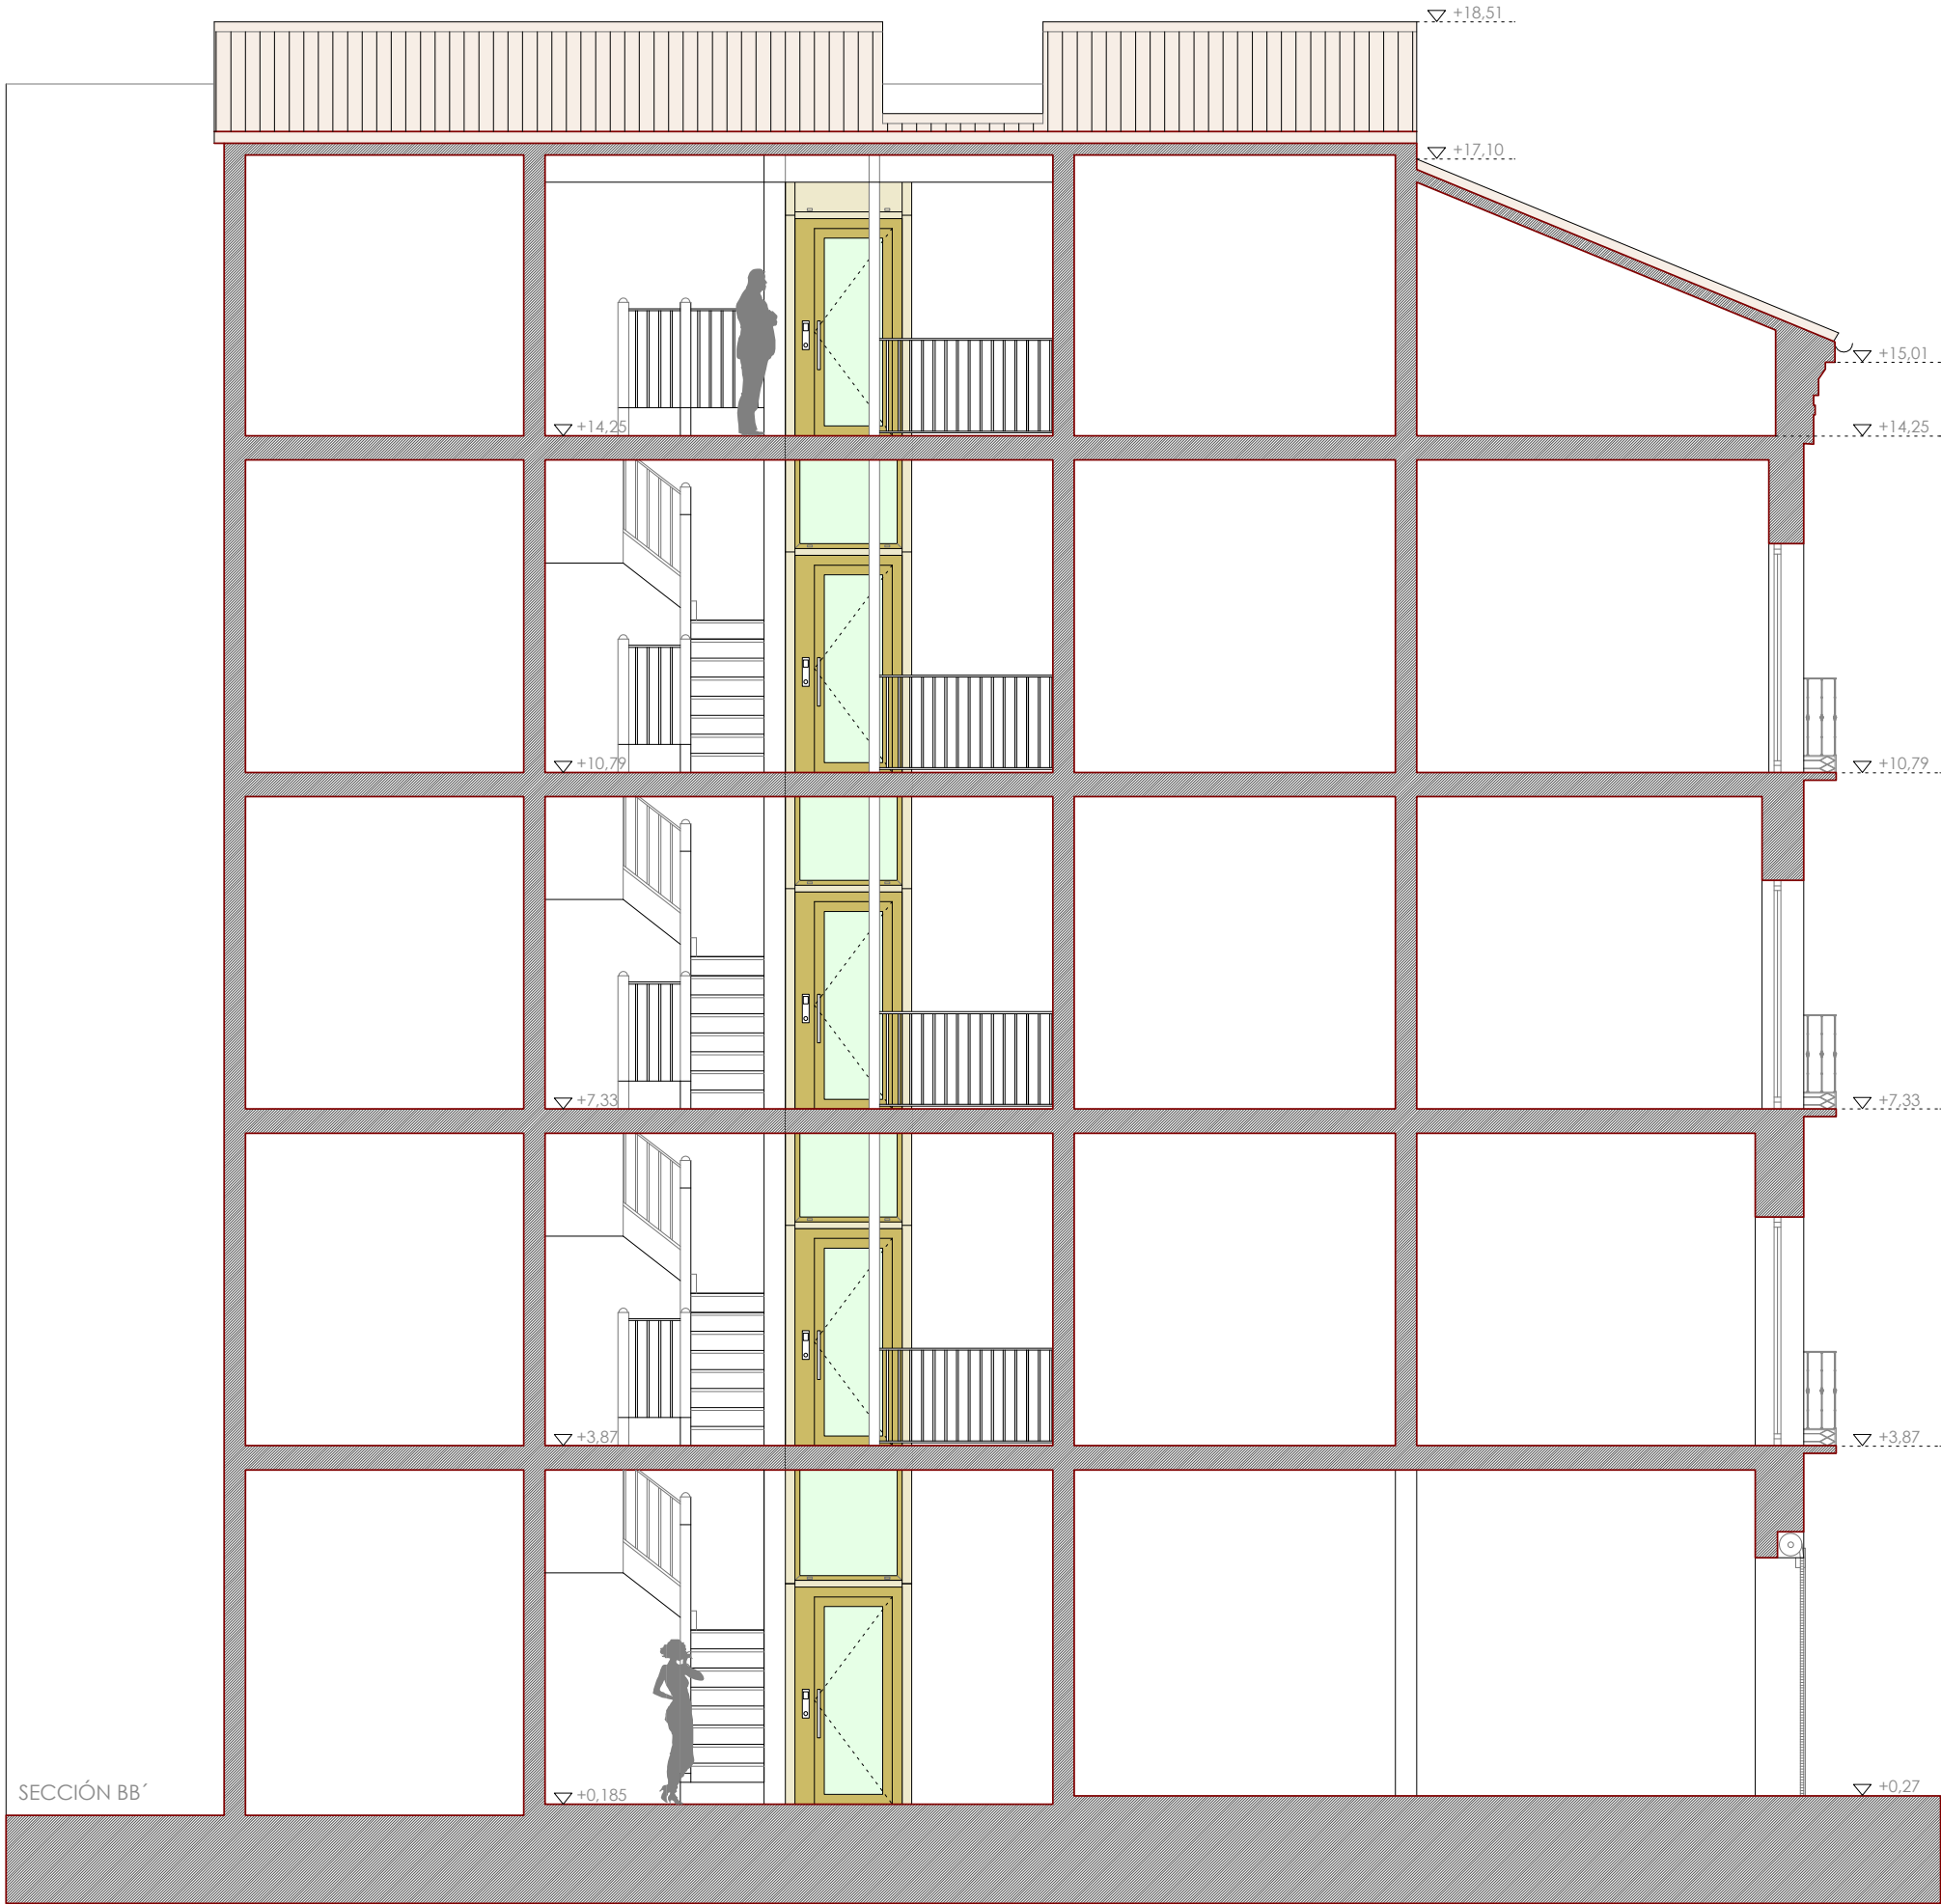

SECCIÓN BB'

Alacet Arquitectura SL, Tr. Cañuelo, 4, Valverde de Alcalá

alacet.

10/01/2025

Proyecto básico de MEJORA DE LA ACCESIBILIDAD UNIVERSAL
Pza. General Vara de Rey, 10, Madrid

propiedad:
C.P. General Vara de Rey, 10

arquitecto:
Luis Fernando Carretero Marco col. 20024

1:75
DIN A3

ESTADO REFORMADO
SECCIONES (II)

A9